Karjääri tn 21a

Paarismaja

Kose alevik, Võru vald, Võru maakond



Aiapoolne vaade ja terrassid

Projekti staadium
Eelprojekt

Projekteerija
Wood NDT OÜ

Ühe korteri netopind
91,4 m^2

Kortereid
2

Ruumid, konstruktsioonid ja tehnosüsteemid. Lisas on eelprojekti plaan, lõiked ja vaated algses A3-formaadis. Visualiseeringud on illustratiivsed.

Üldandmed

Hoone ruumid, konstruktsioonid ja tehnosüsteemid eelprojekti järgi. Andmed on koostatud eelprojekti jooniste ja hoonemudeli põhjal. Konstruktsioonide tabelites on mudelikihid; dokumentide erinevused on selgitatud eraldi.

Näitaja	Andmed
Aadress	Karjääri tn 21a, Kose alevik, Võru vald, Võru maakond, 65601
Katastritunnus	91701:001:3194
Kasutusotstarve	11212 Kahe korteriga elamu
Krundi pindala	1195 m^2
Ehitisealune pind (DWG-vormingus plaani järgi)	239,15 m^2
Netopind, ruumide summa	Korter 1: 91,44 m^2; Korter 2: 91,44 m^2; kokku 182,88 m^2
Köetav pind, põrandaküttega ruumide summa	Korter 1: 91,44 m^2; Korter 2: 91,44 m^2; kokku 182,88 m^2
Köetav pind, eelprojekti koondandmed	183 m^2
Tubade arv korteris	Korter 1: 4; Korter 2: 4
Ruumide arv koos abiruumidega	Korter 1: 9; Korter 2: 9
Laekõrgused (IFC-mudeli ruumide järgi)	2,3 m; 3 m
Projekti staadium	Eelprojekt
Projekteerija	Wood NDT OÜ
Tuleohutusklass	TP3
Hoone kõrgus, eelprojekti järgi	4,4 m
Hoone maht, eelprojekti järgi	1050 m^3
Korruste arv	1
Krundi pindala allikas	EP080926_EP_AA-3-01 seletuskiri (08,09.2026), §2,7, lk 9; asendiplaan EP080926_EP_AS-4-01, tehnilised näitajad
Aia ja parkimiskohtade kasutusõigus	Täpsustub arendajaga
Energiamärgis	Täpsustub arendajaga
Tehnovõrkudega liitumise staatus	Täpsustub arendajaga
Elektrivarustuse faaside arv	Täpsustub arendajaga
Müügiga kaasnevad seadmed ja sisustus	Täpsustub arendajaga
Veearvestuse korraldus	Täpsustub arendajaga

Netopind on hoonemudelis määratud ruumide pindalade summa. Köetavate ruumide pind on seotud põrandakütte tsoonidega; eelprojekti hoone koondpind on esitatud eraldi. Laekõrgus on ruumide tabelis, sh madalam saunalagi. Terrassid ei kuulu ruumide netopinna hulka.

Hoone vaated



Tänavapoolne vaade ja sissepääsud



Korter 1, ruum 1-06. Elutuba/köök, 31,02 m^2



Korter 1, ruum 1-07. Magamistuba I, 13,57 m^2



Vaade kinnistule

Visualiseeringud on illustratiivsed.

Korruse plaan



Korruse plaan

Ruumide mõõdud ja pindalad on järgmises tabelis. Mõõtkavas korruse plaan on dokumendi A3-formaadis jooniste lisas.

Ruumid ja siseviimistlus

Korter 1

Ruum	Pind, m²	Kõrgus, m	Põrandakate
1-01 Esik	8,86	3,0	Keraamiline põrandaplaat
1-02 WC	2,34	3,0	Keraamiline põrandaplaat
1-03 Pesuruum	7,41	3,0	Keraamiline põrandaplaat
1-04 Saun	3,08	2,3	Keraamiline põrandaplaat
1-05 Tehnoruum	4,99	3,0	Keraamiline põrandaplaat
1-06 Elutuba/köök	31,02	3,0	Parketi aluskate 5 mm; Tammeparkett 10 mm
1-07 Magamistuba I	13,57	3,0	Parketi aluskate 5 mm; Tammeparkett 10 mm
1-08 Magamistuba II	9,97	3,0	Parketi aluskate 5 mm; Tammeparkett 10 mm
1-09 Magamistuba III	10,20	3,0	Parketi aluskate 5 mm; Tammeparkett 10 mm
Kokku	**91,44**		

Korter 2

Ruum	Pind, m²	Kõrgus, m	Põrandakate
2-01 Esik	8,86	3,0	Keraamiline põrandaplaat
2-02 WC	2,34	3,0	Keraamiline põrandaplaat
2-03 Pesuruum	7,41	3,0	Keraamiline põrandaplaat
2-04 Saun	3,08	2,3	Keraamiline põrandaplaat
2-05 Tehnoruum	4,99	3,0	Keraamiline põrandaplaat
2-06 Elutuba/köök	31,02	3,0	Parketi aluskate 5 mm; Tammeparkett 10 mm
2-07 Magamistuba I	13,57	3,0	Parketi aluskate 5 mm; Tammeparkett 10 mm
2-08 Magamistuba II	9,97	3,0	Parketi aluskate 5 mm; Tammeparkett 10 mm
2-09 Magamistuba III	10,20	3,0	Parketi aluskate 5 mm; Tammeparkett 10 mm
Kokku	**91,44**		

Põrandakatete nimetused pärinevad IFC-mudeli materjalikataloogist. Kihtide paksused on konstruktsioonide tabelites. Üksikpinnad on ümardatud; kogupind on arvutatud ümardamata tabeliandmetest.

Seinaviimistlus märgades ruumides

Ruum	Materjal	Viimistluse kõrgus, m
1-02 / 2-02 WC	Keraamiline seinaplaat	1,2
1-03 / 2-03 Pesuruum	Keraamiline seinaplaat	3
1-04 / 2-04 Saun	Saunavooder (haab)	2,3

Välissein ja räästas

VS-1. Puitkarkass-välissein

Kogupaksus 356 mm

Kiht	Materjal	Paksus, mm
Vertikaalne laudis 28×195 mm	Välisvoodrilaud 28×195, naturaalne puit	28
Horisontaalne distantsliist 25×50 mm s400	Distantsliist (kuusk)	25
Vertikaalne distantsliist 22×50 mm s600	Distantsliist (kuusk)	22
Tuuletõkkeplaat 9	Tuuletõkkeplaat 9 mm	9
Puitkarkass 45×195 mm s600 / mineraalvill 200	Mineraalvill	195
Aurutõkkemembraan	Aurutõkkekile	1
Distantsliist 50×50 mm / mineraalvill 50	Mineraalvill	50
Kipsplaat 13	Kipsplaat 13 mm	13
Kipsplaat 13 + siseviimistlus	Kipsplaat 13 mm, värvitud	13
Kihid kokku		**356 mm**

Kihid on IFC materjalikihtide järjekorras; VS-1 ja RV-1 väljast sisse. Heliisolatsioon, mudelis deklareeritud: R'tr,s,w 35 dB.

RV-1 Räästavöö / rinnatis

Kogupaksus 306 mm

Kiht	Materjal	Paksus, mm
Vertikaalne laudis 28×195 mm tumehall	Välisvoodrilaud 28×195, tumehall	28
Horisontaalne distantsliist 25×50 mm s400	Distantsliist (kuusk)	25
Vertikaalne distantsliist 22×50 mm s600	Distantsliist (kuusk)	22
Tuuletõkkeplaat 9	Tuuletõkkeplaat 9 mm	9
Puitkarkass 45×195 mm	Mineraalvill	195
OSB 22	OSB-plaat 22 mm	22
SBS ülespööre	SBS-rullkate	5
Kihid kokku		**306 mm**

Kihid on IFC materjalikihtide järjekorras; VS-1 ja RV-1 väljast sisse.

Korteritevaheline sein ja vaheseinad

EI 30 Korteritevaheline sein

Kogupaksus 272 mm

Kiht	Materjal	Paksus, mm
Kipsplaat 13 + siseviimistlus	Kipsplaat 13 mm, värvitud	13
Kipsplaat 13	Kipsplaat 13 mm	13
Puitkarkass 45×95 mm / mineraalvill 100	Mineraalvill	95
Õhkvahe 30	Õhkvahe	30
Puitkarkass 45×95 mm / mineraalvill 100	Mineraalvill	95
Kipsplaat 13	Kipsplaat 13 mm	13
Kipsplaat 13 + siseviimistlus	Kipsplaat 13 mm, värvitud	13
Kihid kokku		**272 mm**

Kihid on IFC materjalikihtide järjekorras; VS-1 ja RV-1 väljast sisse. Tulepüsivus: EI 30 (mudelis deklareeritud).

SS-1. Metallkarkassiga sisesein

Kogupaksus 92 mm

Kiht	Materjal	Paksus, mm
Kipsplaat 13 + siseviimistlus	Kipsplaat 13 mm, värvitud	13
Metallkarkass 66 s400 / mineraalvill 70	Mineraalvill	66
Kipsplaat 13 + siseviimistlus	Kipsplaat 13 mm, värvitud	13
Kihid kokku		**92 mm**

Kihid on IFC materjalikihtide järjekorras; VS-1 ja RV-1 väljast sisse. Heliisolatsioon, mudelis deklareeritud: R'w 43 dB.

Katus ja põrand

K – katus (kalle 2°)

Kogupaksus täpsustub tööprojektis

Kiht	Materjal	Paksus, mm
SBS-kate (2 kihti)	SBS-rullkate	8
OSB 22	OSB-plaat 22 mm	22
Distantsliist 45×45 mm (tuulutusvahe)	Distantsliist (kuusk)	45
Katuse aluskate	Katuse aluskate	2
Puitferm F04	täpsustub tööprojektis	täpsustub tööprojektis
Puitferm F03	täpsustub tööprojektis	täpsustub tööprojektis
Puitferm F02	täpsustub tööprojektis	täpsustub tööprojektis
Puitferm F01	täpsustub tööprojektis	täpsustub tööprojektis
Puitferm F16	täpsustub tööprojektis	täpsustub tööprojektis
Puitferm F15	täpsustub tööprojektis	täpsustub tööprojektis
Puitferm F14	täpsustub tööprojektis	täpsustub tööprojektis
Puitferm F13	täpsustub tööprojektis	täpsustub tööprojektis
Puitferm F12	täpsustub tööprojektis	täpsustub tööprojektis
Puitferm F11	täpsustub tööprojektis	täpsustub tööprojektis
Puitferm F10	täpsustub tööprojektis	täpsustub tööprojektis
Puitferm F09	täpsustub tööprojektis	täpsustub tööprojektis

Kiht	Materjal	Paksus, mm
Puitferm F08	täpsustub tööprojektis	täpsustub tööprojektis
Puitferm F07	täpsustub tööprojektis	täpsustub tööprojektis
Puitferm F06	täpsustub tööprojektis	täpsustub tööprojektis
Puitferm F05	täpsustub tööprojektis	täpsustub tööprojektis
Kihid kokku		**täpsustub tööprojektis**

Katusekatte ja aluse kihtide paksused on mõõdetud IFC-mudeli profiililt vertikaalsuunas. Kandekonstruktsioon on muutuva kõrgusega puitferm; fermide kõrgust ei ole liidetud kihtide summasse. Soojustatud lagi on VL-1 tabelis.

Katusekate: SBS, tumehall.

Puitfermi osad: alumine vöö 45×175 mm; diagonaalid ja postid 45×70 mm; ülemvöö 45×95 mm.

P – aluspõrand ja plaatvundament

Kogupaksus täpsustub tööprojektis

Kiht	Materjal	Paksus, mm
Põrandaviimistluse kiht	Ruumide tabeli järgi	15
Põrand 1-09 Magamistuba III	Parketi aluskate 5 mm; Tammeparkett 10 mm	15
Põrand 1-02 WC	Keraamiline põrandaplaat	15
Põrand 2-07 Magamistuba I	Parketi aluskate 5 mm; Tammeparkett 10 mm	15
Põrand 2-06 Elutuba/köök	Parketi aluskate 5 mm; Tammeparkett 10 mm	15
Põrand 1-03 Pesuruum	Keraamiline põrandaplaat	15
Põrand 2-09 Magamistuba III	Parketi aluskate 5 mm; Tammeparkett 10 mm	15
Põrand 2-04 Saun	Keraamiline põrandaplaat	15
Põrand 1-08 Magamistuba II	Parketi aluskate 5 mm; Tammeparkett 10 mm	15
Põrand 1-01 Esik	Keraamiline põrandaplaat	15
Põrand 1-05 Tehnoruum	Keraamiline põrandaplaat	15
Põrand 2-01 Esik	Keraamiline põrandaplaat	15
Põrand 2-08 Magamistuba II	Parketi aluskate 5 mm; Tammeparkett 10 mm	15
Põrand 2-02 WC	Keraamiline põrandaplaat	15
Põrand 2-05 Tehnoruum	Keraamiline põrandaplaat	15
Põrand 2-03 Pesuruum	Keraamiline põrandaplaat	15
Põrand 1-06 Elutuba/köök	Parketi aluskate 5 mm; Tammeparkett 10 mm	15
Põrand 1-07 Magamistuba I	Parketi aluskate 5 mm; Tammeparkett 10 mm	15
Põrand 1-04 Saun	Keraamiline põrandaplaat	15
Raudbetoon 100 + põrandaküttetorud	Raudbetoon C25/30	100
L-servaelement EPS 100 (püstosa)	Vahtpolüstüreen EPS	302
Hüdroisolatsioon	Hüdroisolatsioon	2
Vahtpolüstüreen EPS 300	Vahtpolüstüreen EPS	300
Hüdroisolatsioon servatala all	Hüdroisolatsioon	2
L-servaelement EPS 100 (tald)	Vahtpolüstüreen EPS	100
Geotekstiil	Geotekstiil	2
Tihendatud liiv 300	Tihendatud liiv	täpsustub tööprojektis
Kihid kokku		**täpsustub tööprojektis**

Paksused pärinevad IFC-mudeli geomeetriast. Parketi aluskatte ja hüdroisolatsiooni paksus on mudeli eeldus. Põrandaviimistluse mudelikiht hõlmab kogu viimistlusele määratud paksust. Servatala ja perimeetrisoojustus on eraldi detailid.

Servatala RB 400×300 mm (plaadiga).

Lagi ja soojustus

VL-1 – soojustatud lagi

Kogupaksus täpsustub tööprojektis

Kiht	Materjal	Paksus, mm
Lagi VL-1 Korter 1	Aurutõke; Distantsliist 18×95 mm; Kipsplaat; Puistevill; Roov 45×45 mm; Siseviimistlus	täpsustub tööprojektis
Lae roov ja distantsliist Korter 1	Distantsliist (kuusk)	63
Lae aurutõke Korter 1	Aurutõkkekile	1
Puistevill 600 Korter 1	Puistevill	600
Kihid kokku		**täpsustub tööprojektis**

Alt üles, mõlemal korteril sama; tabelis korteri 1 näide. Roov ja distantsliist on koondkihina.
Puistevill paikneb fermide vahel ja peal; saunal on eraldi madalam puitlagi.

Soojustuskihid

Tarind	Soojustus / projekti tähistus	Mudelikihi paksus, mm
VS-1	Puitkarkass 45×195 mm s600 / mineraalvill 200	195
VS-1	Distantsliist 50×50 mm / mineraalvill 50	50
RV-1	Puitkarkass 45×195 mm	195
EI 30	Puitkarkass 45×95 mm / mineraalvill 100	95
EI 30	Puitkarkass 45×95 mm / mineraalvill 100	95
SS-1	Metallkarkass 66 s400 / mineraalvill 70	66
P	L-servaelement EPS 100 (püstosa)	302
P	Vahtpolüstüreen EPS 300	300
P	L-servaelement EPS 100 (tald)	100
VL-1	Lagi VL-1 Korter 1	täpsustub tööprojektis
VL-1	Puistevill 600 Korter 1	600
Perimeeter	Perimeetrisoojustus EPS Perimeter 120, 100 mm, 1 m, kalle 2 %	täpsustub tööprojektis

Seinte villakihi nimetus võib sisaldada nimipaksust (200, 100 või 70 mm); tabeli paksus on IFC tarindikihi mõõt (195, 95 või 66 mm). Korduvad read tähistavad eraldi kihte.

Soojusläbivus

Tarind	U, W/(m²·K), eelprojekti järgi
VS-1	0,16

Tarind	U, W/(m²·K), eelprojekti järgi
P	0,11

U-väärtused on ainult eelprojektis deklareeritud väärtused. Muude tarindite soojusnäitajad täpsustuvad tööprojektis.

Arhitekti dokumendid ja BIM-mudel

Tarind	Seletuskirja väärtus	BIM-mudeli väärtus / märkus
VS-1 mineraalvill	200 + 50 mm (§4,4, lk 13)	195 + 50 mm; 195 mm karkassikiht
SS-1 mineraalvill	66 mm (§4,4, lk 13)	66 mm; kihi nimetuses nimipaksus 70 mm
Põranda EPS	300 mm (§4,3, lk 13)	300 mm; servatala L-elemendid EPS 100 (püstosa ja tald)
Sokkel ja perimeeter	EPS 100 mm; horisontaalne perimeetrisoojustus 100 mm, laius 1,0 m (§4,3, lk 12)	Vaata mudelikihtide tabelit
Lae puistevill	600 mm; U = 0,07 W/(m^2·K)(§4,4, lk 14)	600 mm; mõlemal korteril sama lae konstruktsioon
Akna U-väärtus	0,8 W/(m^2·K)(§4,4, lk 14)	0,8 W/(m^2·K); kogu akna deklareeritud väärtus
Sisepindade tuletundlikkus	Seinad ja lagi D-s2,d2; tehnoruum ning terrassi vaheseinad B-s1,d0 (§5,4, lk 16)	VS-1 tähisel D-s2,d2; see ei ole tulepüsivuse kestus
Korteritevahelise seina tulepüsivus	Seletuskiri EI 30 väärtust ei määra	EI 30 on mudeli deklaratsioon

Allikas: EP080926_EP_AA-3-01 seletuskiri (08,09.2026).

Avatäited

Mõõdud on IFC avatäite üldmõõdud. Kogused on korterite kaupa. U-väärtused on esitatud eelprojekti järgi; kriips tähendab, et väärtust ei ole deklareeritud.

Avatäide	Laius × kõrgus, mm	Korter 1	Korter 2	U, W/(m²·K)
Aken 1600×2000 mm	1600 × 2000	2	2	0,8
Välisuks	1000 × 2600	1	1	1
Terrassiuks	1600 × 2600	2	2	1
Terrassiuks	2600 × 2600	1	1	1
Klaasuks	900 × 2600	1	1	1
Siseuks	800 × 2100	6	6	-
Saunauks (klaas) 700×2100 mm	700 × 2100	1	1	-

Materjalid ja viimistlus

Avatäide	IFC-mudeli materjalid
Aken 1600×2000 mm	Kipsplaat 13 mm, värvitud; Klaaspakett 3-kordne; Kroom; PVC-raam, antratsiit; Plekk, tumehall; Põrandaliist, valge; Vahtpolüstüreen EPS
Klaasuks	Kipsplaat 13 mm, värvitud; Klaaspakett 3-kordne; Kroom; PVC-raam, antratsiit; Plekk, tumehall; Roostevaba teras
Saunauks (klaas) 700×2100 mm	Kroom; Saunaukse klaas, pronks; Saunavooder (haab)
Siseuks	Kroom; Siseuks, valge MDF
Terrassiuks	Kipsplaat 13 mm, värvitud; Klaaspakett 3-kordne; Kroom; PVC-raam, antratsiit; Plekk, tumehall; Roostevaba teras
Välisuks	Kipsplaat 13 mm, värvitud; Klaaspakett 3-kordne; Kroom; PVC-raam, antratsiit; Plekk, tumehall; Roostevaba teras; Välisuks, antratsiit

Tehnosüsteemid

Tehnosüsteemid on eelprojekti lahendus. Lõplikud seadmed, võimsused, liitumistingimused ja juhtimine täpsustuvad tööprojektis.

Seadmed korterite kaupa

Seade	Eelprojektis määratud andmed
Korter 1 Elektrikeris 8 kW	Võimsus: 8 kW
Korter 1 Integreeritud ahi	
Korter 1 Integreeritud külmik-sügavkülmik	
Korter 1 Integreeritud nõudepesumasin	
Korter 1 Jahutusseadme siseseade (laekassett)	Jahutusvõimsus: 3,5 kW
Korter 1 Maasoojuspump 8 kW + 180 l boiler	Võimsus: 8 kW; Boiler: 180 l; Näidisseade: Nibe S1255-8 (lõplik valik täpsustub tööprojektis)
Korter 1 Peakilp	Peakaitse: 25 A
Korter 1 Ventilatsiooniseade Systemair SAVE VTR 250/B	Õhuhulk, mudeli deklaratsioon: 50 l/s; Soojustagastuse kasutegur, mudeli deklaratsioon: 85 %
Korter 2 Elektrikeris 8 kW	Võimsus: 8 kW
Korter 2 Integreeritud ahi	
Korter 2 Integreeritud külmik-sügavkülmik	
Korter 2 Integreeritud nõudepesumasin	
Korter 2 Jahutusseadme siseseade (laekassett)	Jahutusvõimsus: 3,5 kW
Korter 2 Maasoojuspump 8 kW + 180 l boiler	Võimsus: 8 kW; Boiler: 180 l; Näidisseade: Nibe S1255-8 (lõplik valik täpsustub tööprojektis)
Korter 2 Peakilp	Peakaitse: 25 A
Korter 2 Ventilatsiooniseade Systemair SAVE VTR 250/B	Õhuhulk, mudeli deklaratsioon: 50 l/s; Soojustagastuse kasutegur, mudeli deklaratsioon: 85 %
Seletuskiri (§6,1–6,2, lk 20)	**BIM-mudel / selgitus**
Soojuspumba koguvõimsus ligikaudu 8 kW	Mudelis maasoojuspump 8 kW korteri kohta; võimsuse ulatus erineb seletuskirjast
Systemair SAVE või sarnane; soojustagastuse kasutegur kuni 85 %	Mudelis deklareeritud kasutegur 85 % ja seadme õhuhulk 50 l/s korteri kohta
Ventilatsiooni õhuhulgad ei ole määratud	Mudeli sissepuhke summaks 52 l/s; väljatõmbe summaks 37 l/s ning kubu nimetuses 10 l/s. Töörežiimid vajavad projekteerija täpsustust
Eraldi jahutusseade, siseosa koridoris ja välisosad hoone küljel	Eraldi split-jahutus: laekassett 3,5 kW ja seotud välisseade korteri kohta

Süsteemid

Korterite korduvad süsteeminimetused on koondatud.

Valdkond	Mudelis määratud süsteemid
Küte	Küttesõlm (SP → kollektor); Maakollektor (soolvesi); Põrandaküte
Ventilatsioon	Heitõhk (H); Sissepuhe (S); Välisõhk (VÄ); Väljatõmme (V)
Jahutus	Jahutus (split)
Vesi ja kanalisatsioon	Drenaaž; Kanalisatsioon (K1); Kanalisatsiooni liitumine; Kanalisatsiooni tuulutus; Külm tarbevesi (V1); Sadevesi; Soe tarbevesi (V3); Veevarustuse liitumine
Elekter	Elekter; Elektriliitumine; Valgustus

Tehnosüsteemide materjalid ja ühendused

Eelprojekti torustike, ventilatsioonikanalite ja elektrivarustuse andmed. Läbimõõdud on mudelis deklareeritud mõõdud; isolatsioon ja toru nimetus on esitatud materjaliveerus. Sama tüüpi valgustusharud on koondatud.

Süsteem	Materjal / projekti tähistus	Läbimõõdud, mm
Drenaažitoru	PVC-drenaažitoru, killustikus	110
Heitõhk	Tsinkplekk + 50 mm isolatsioon	160
Kanalisatsioon	PP 110	50, 110
Kanalisatsiooni liitumine PVC160	Oranž PVC-kanalisatsioonitoru	160
Külm vesi	PEX 20 toru-torus	20, 25, 32
Külmaainetorud (isol.)	Külmaainetoru (vask, isol.)	35
Kütte pealevool	Cu 28 isol.	20, 28, 32
Kütte tagasivool	Cu 28 isol.	20, 28, 32
SADE sadeveetoru PVC110	PVC-U DN/OD110 SN8; kalle 1,5 %	110
Sissepuhe	Tsingitud plekist spiraaltoru + 50 mm isolatsioon	125, 160
Soe vesi	PEX 20 toru-torus	20, 25, 32
Toitekaabel AXPK 4×35 mm	Elektrikaabel	30
Valgustuse harud 3G1,5	MMJ 3G1,5 mm^2	9
Veesisend PE32	PE 32 SDR11	32
Veevarustuse liitumine PE40	Külm vesi PEX	40
Vihmaveetoru SK-01	Sadevesi, plekk tumehall	100
Vihmaveetoru SK-02	Sadevesi, plekk tumehall	100
Vihmaveetoru SK-03	Sadevesi, plekk tumehall	100
Vihmaveetoru SK-04	Sadevesi, plekk tumehall	100
Välisõhk	Tsinkplekk + 50 mm isolatsioon	160
Väljatõmme	Tsingitud plekist spiraaltoru + 50 mm isolatsioon	100, 125, 160

Maasoojuskollektor

Korter	Eelprojekti lahendus
Korter 1	PE 40×2,4 mm, PN 6; sügavus 1,2 m; samm 0,8 m; pikkus, mudeli deklaratsioon 312 m; soolvesi: etanool 28 %
Korter 2	PE 40×2,4 mm, PN 6; sügavus 1,2 m; samm 0,8 m; pikkus, mudeli deklaratsioon 312 m; soolvesi: etanool 28 %
Allikas	**Täpsustus**
Seletuskiri, §6	Maakollektori sügavust, pikkust ja torutähist PE40/PEX ei ole määratud

Allikas	Täpsustus
Maakollektor, BIM-mudel	Deklaratsioon: sügavus 1,2 m ja pikkus 312 m korteri kohta. Geomeetrias põhivälja telg –1,200 m põrandast ehk 1,000 m mudeli maapinnast; torutee ligikaudu 309,32 m. Need on erineva alusega mudeliandmed
Veevarustuse ühendus, BIM-mudel	Nimetus PE40 ja läbimõõt 40 mm; materjalikataloogis „Külm vesi PEX". Materjalide vastuolu vajab projekteerija täpsustust

Liitumiskilp (2 arvestit).

Küte: ruumipõhine juhtimine

Põrandaküte on allpool loetletud ruumides, eraldi ruumipõhiste tsoonide ja kütteringidega. Ruumide termostaatjuhtimine on näidatud mudeli järgi; sauna eraldi termostaat täpsustub tööprojektis.

Korter 1

Ruum	Kütteringid	Samm, mm	Seadistatud temperatuur, °C	Eraldi termostaat
1-01 Esik	03, 04	150	21	Jah
1-02 WC	09	100	24	Jah
1-03 Pesuruum	07, 08	100	24	Jah
1-04 Saun	06	150	24	täpsustub tööprojektis
1-05 Tehnoruum	01	200	21	Jah
1-06 Elutuba/köök	10, 11, 12	200	21	Jah
1-07 Magamistuba I	13	200	21	Jah
1-08 Magamistuba II	02	200	21	Jah
1-09 Magamistuba III	05	200	21	Jah

Korter 2

Ruum	Kütteringid	Samm, mm	Seadistatud temperatuur, °C	Eraldi termostaat
2-01 Esik	03, 04	150	21	Jah
2-02 WC	09	100	24	Jah
2-03 Pesuruum	07, 08	100	24	Jah
2-04 Saun	06	150	24	täpsustub tööprojektis
2-05 Tehnoruum	01	200	21	Jah
2-06 Elutuba/köök	10, 11, 12	200	21	Jah
2-07 Magamistuba I	13	200	21	Jah
2-08 Magamistuba II	02	200	21	Jah
2-09 Magamistuba III	05	200	21	Jah

Välisviimistlus ja dokumendid

Fassaad

- Välisvoodrilaud 28×195, naturaalne puit
- Välisvoodrilaud 28×195, tumehall
- Välisvoodrilaud 28×195, tumepruun

Õueala ja sokkel


- Betoonkivisillutis (2 parkimiskohta korteri kohta ja kõnniteed)
- Keevispaneelaed, kõrgus 1,5 m
- Sokliplaat 10 mm
- Korteri 1 terrass
- Korteri 2 terrass
- Korteri 1 välistrepp / varikatusealune
- Korteri 2 välistrepp / varikatusealune

Dokumendid

- Joonised: plaan, lõiked ja vaated (PDF)
- 360° virtuaaltuur
- Interaktiivne 3D-mudel
- BIM-mudel (IFC)
- Lae alla IFC (IFC4)

Visualiseeringud on illustratiivsed ja põhinevad eelprojektil. Õueala kirjeldus näitab projekti lahendust; kasutusõigused on toodud üldandmetes.

1. KORRUSE PLAAN

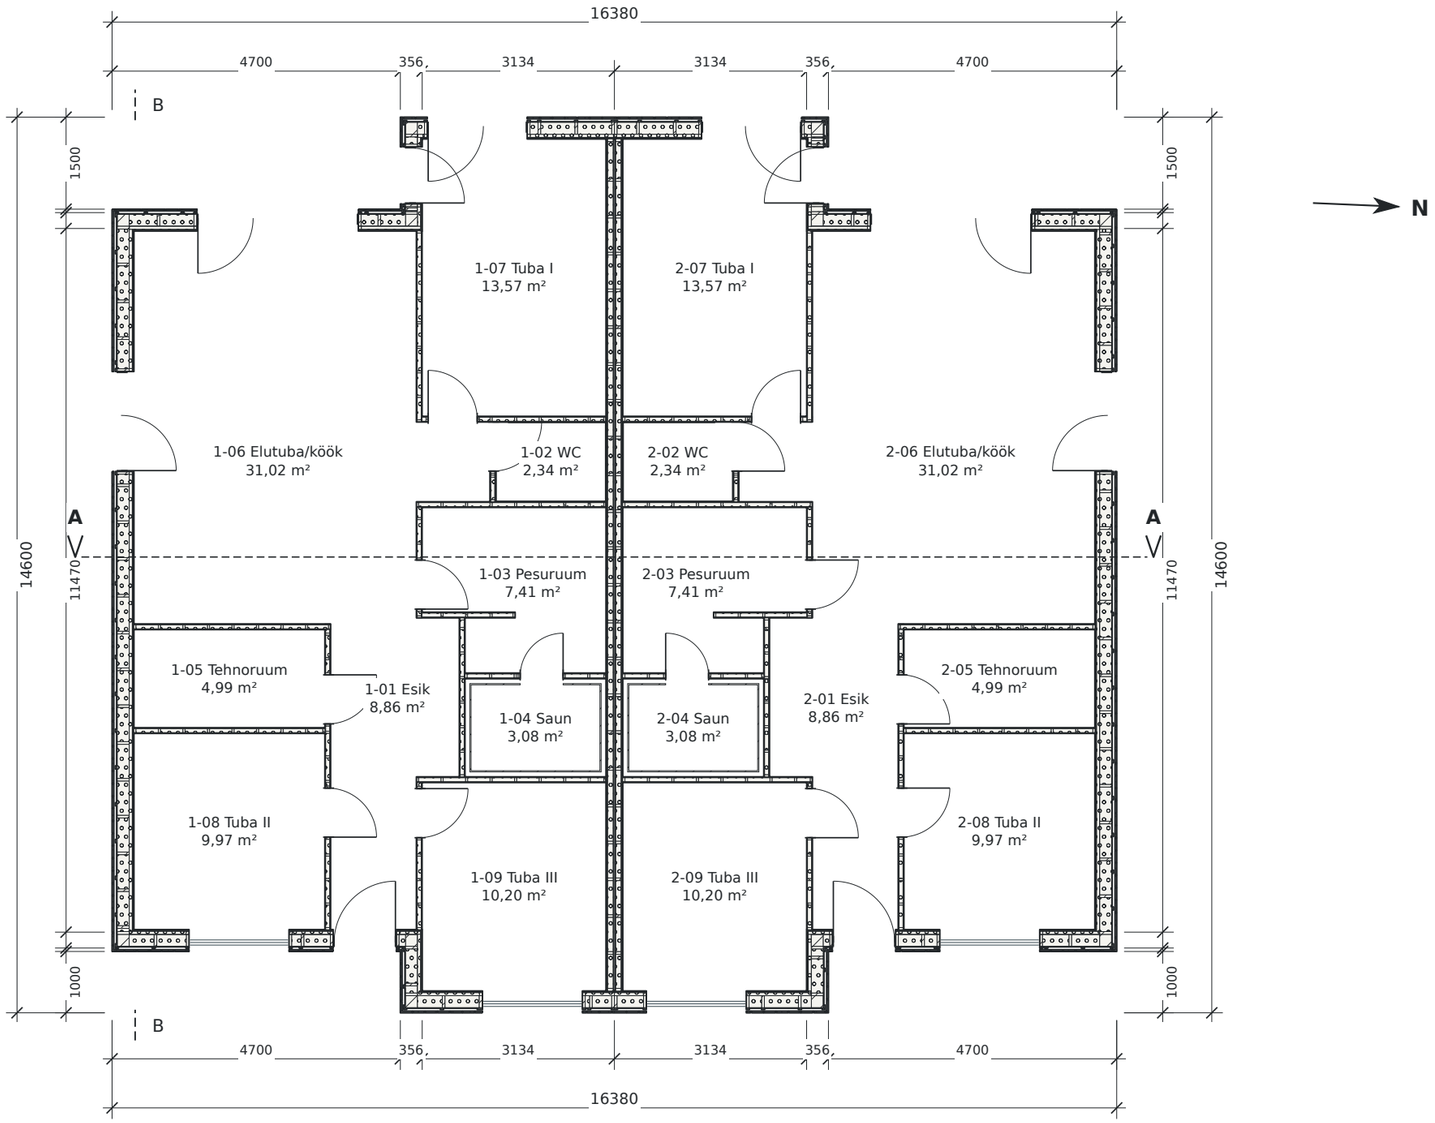

0 1 2 5 m

1:100

RUUMIDE EKSPLIKATSIOON

KRT 1		m²
1-01	Esik	8,86
1-02	WC	2,34
1-03	Pesuruum	7,41
1-04	Saun	3,08
1-05	Tehnoruum	4,99
1-06	Elutuba/köök	31,02
1-07	Tuba I	13,57
1-08	Tuba II	9,97
1-09	Tuba III	10,20
KOKKU		**91,44**

KRT 2		m²
2-01	Esik	8,86
2-02	WC	2,34
2-03	Pesuruum	7,41
2-04	Saun	3,08
2-05	Tehnoruum	4,99
2-06	Elutuba/köök	31,02
2-07	Tuba I	13,57
2-08	Tuba II	9,97
2-09	Tuba III	10,20
KOKKU		**91,44**

TINGMÄRGID

- Puitkarkass / laudis
- Mineraalvill
- Kipsplaat

Lõiketasapind +1.000 m
Ruumide pind: IFC netopind
A-A / B-B: vt leht A-02

IFC4 / ARHITEKTUUR

Mõõdud millimeetrites; kõrgused meetrites.

A3 · Prindi 100% · Ära sobita lehele

EP080926 Paarismaja Karjääri tn 21a


Karjääri tn 21a, Kose alevik, Võru vald, Võru maakond

1. korruse plaan — Eelprojekt


PROJEKTEERIJA	KUUPÄEV	MÕÕTKAVA	LEHT
Wood NDT OÜ	2026-10-28	1:100	A-01

LÕIKED A-A JA B-B

A-A / LÄBI MÕLEMA KORTERI

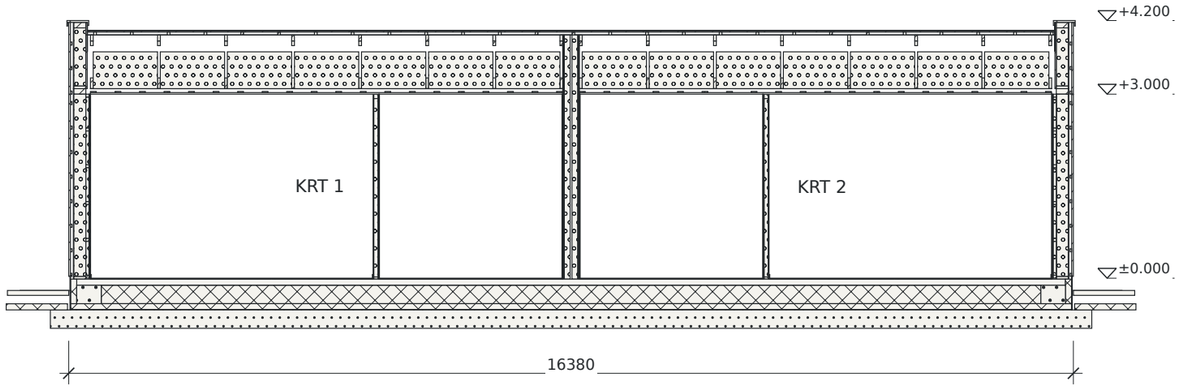

B-B / PIKILÕIGE FERMI TASAPINNAS

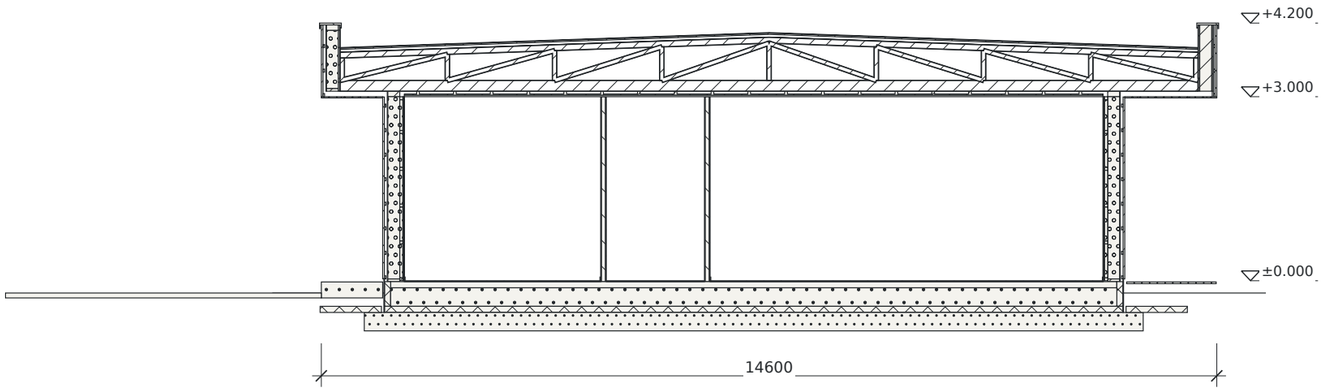

0 1 2 5 m

1:100

KONSTRUKTSIOONID

- Puitkarkass / fermid
- Mineraalvill
- Puistevill
- EPS-soojustus
- Raudbetoon
- Tihendatud liiv
- Kipsplaat

KÕRGUSSÜSTEEM

±0.000 = 86.30 m EH2000
Valmis põrand: ±0.000
Maapind: -0.200

LÕIKETASAPINNAD

A-A: mudeli Y = 7.430 m
B-B: mudeli X = 0.376 m
Lõikesuunad: vt plaan A-01

Fermid ja kihid: IFC geomeetria.
Viirutus tähistab lõigatud materjali.
Kõik mõõtkavad 1:100.

IFC4 / ARHITEKTUUR

Mõõdud millimeetrites; kõrgused meetrites.

A3 · Prindi 100% · Ära sobita lehele

EP080926 Paarismaja Karjääri tn 21a


Karjääri tn 21a, Kose alevik, Võru vald, Võru maakond

Lõiked A-A ja B-B — Eelprojekt

PROJEKTEERIJA	KUUPÄEV	MÕÕTKAVA	LEHT
Wood NDT OÜ	2026-10-28	1:100	A-02


VAATED

VAADE / IDA

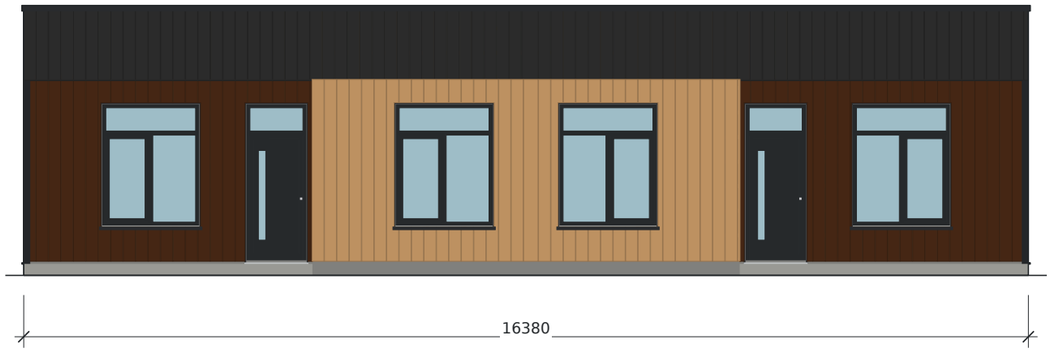


Põrand ±0.000 / Rinnatis +4.200

VAADE / LÕUNA

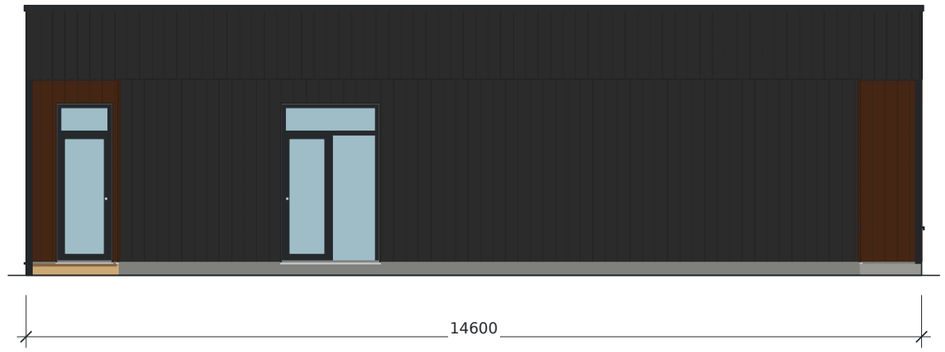


Põrand ±0.000 / Rinnatis +4.200

VAADE / LÄÄS

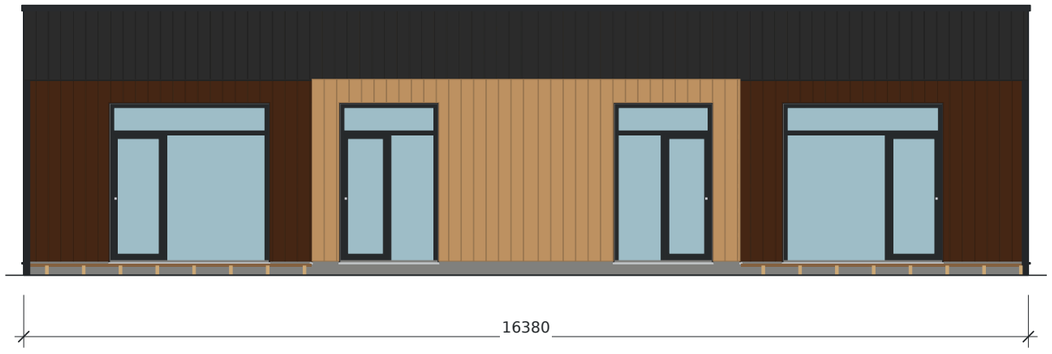

Põrand ±0.000 / Rinnatis +4.200

VAADE / PÕHI

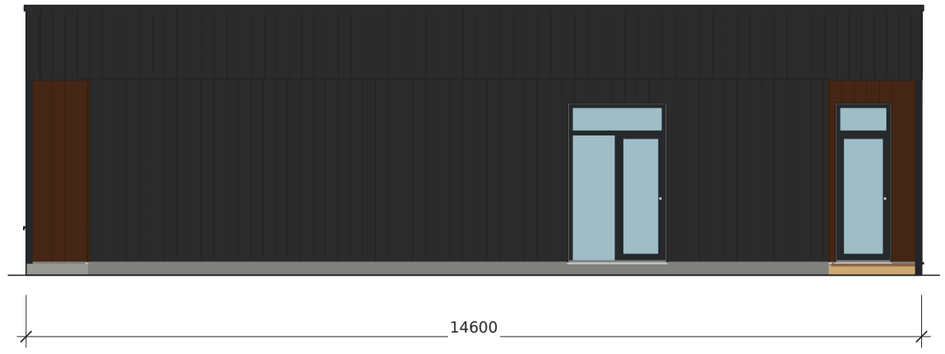

Põrand ±0.000 / Rinnatis +4.200

VÄLISVIIMISTLUS

- Naturaalne puit
- Tumepruun laudis
- Tumehall laudis
- Antratsiit raamid

IFC4 / ARHITEKTUUR

Mõõdud millimeetrites; kõrgused meetrites.

A3 · Prindi 100% · Ära sobita lehele

EP080926 Paarismaja Karjääri tn 21a

Karjääri tn 21a, Kose alevik, Võru vald, Võru maakond

Vaated — Eelprojekt

PROJEKTEERIJA	KUUPÄEV	MÕÕTKAVA	LEHT
Wood NDT OÜ	2026-10-28	1:100	A-03