
1. KORRUSE PLAAN

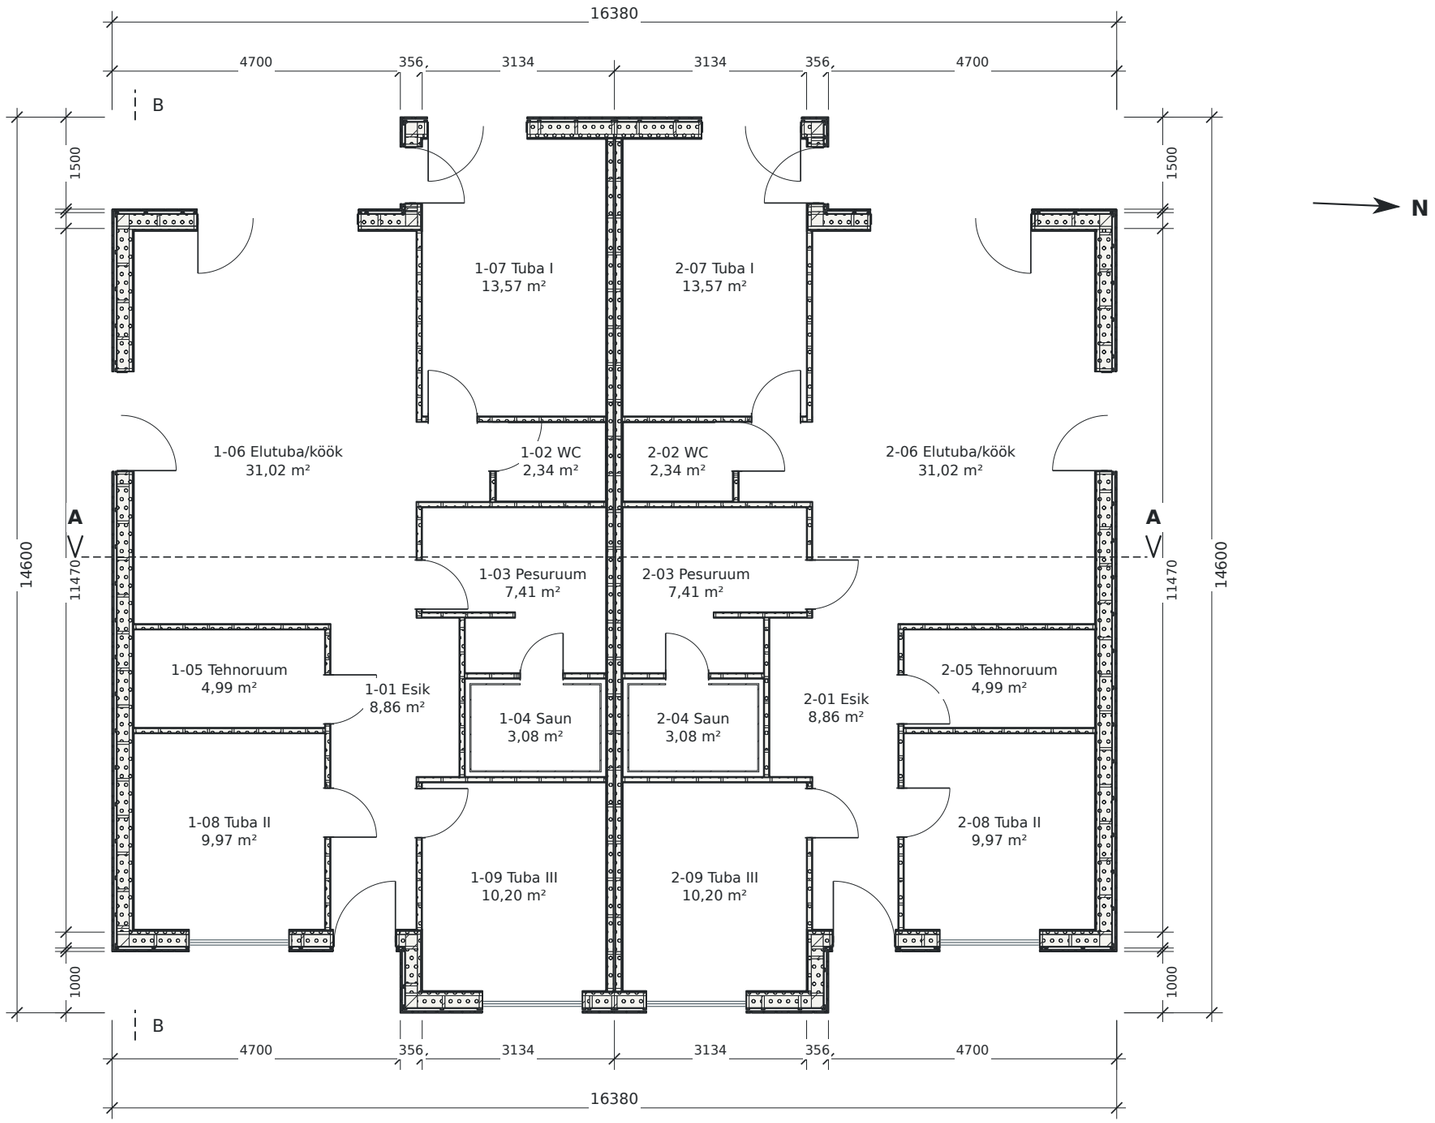

0 1 2 5 m

1:100

RUUMIDE EKSPLIKATSIOON

KRT 1		m²
1-01	Esik	8,86
1-02	WC	2,34
1-03	Pesuruum	7,41
1-04	Saun	3,08
1-05	Tehnoruum	4,99
1-06	Elutuba/köök	31,02
1-07	Tuba I	13,57
1-08	Tuba II	9,97
1-09	Tuba III	10,20
KOKKU		**91,44**

KRT 2		m²
2-01	Esik	8,86
2-02	WC	2,34
2-03	Pesuruum	7,41
2-04	Saun	3,08
2-05	Tehnoruum	4,99
2-06	Elutuba/köök	31,02
2-07	Tuba I	13,57
2-08	Tuba II	9,97
2-09	Tuba III	10,20
KOKKU		**91,44**

TINGMÄRGID

- Puitkarkass / laudis
- Mineraalvill
- Kipsplaat

Lõiketasapind +1.000 m
Ruumide pind: IFC netopind
A-A / B-B: vt leht A-02

IFC4 / ARHITEKTUUR

Mõõdud millimeetrites; kõrgused meetrites.

A3 · Prindi 100% · Ära sobita lehele

EP080926 Paarismaja Karjääri tn 21a


Karjääri tn 21a, Kose alevik, Võru vald, Võru maakond

1. korruse plaan — Eelprojekt


PROJEKTEERIJA	KUUPÄEV	MÕÕTKAVA	LEHT
Wood NDT OÜ	2026-10-28	1:100	A-01

LÕIKED A-A JA B-B

A-A / LÄBI MÕLEMA KORTERI

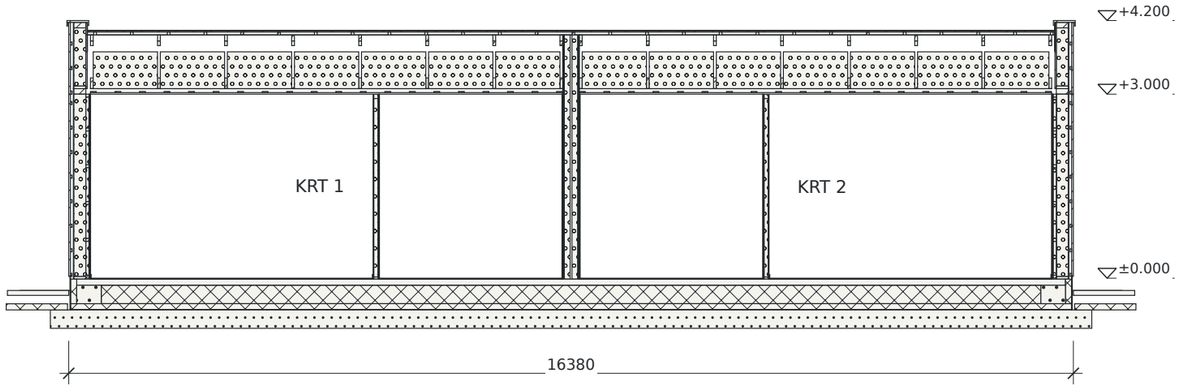

B-B / PIKILÕIGE FERMI TASAPINNAS

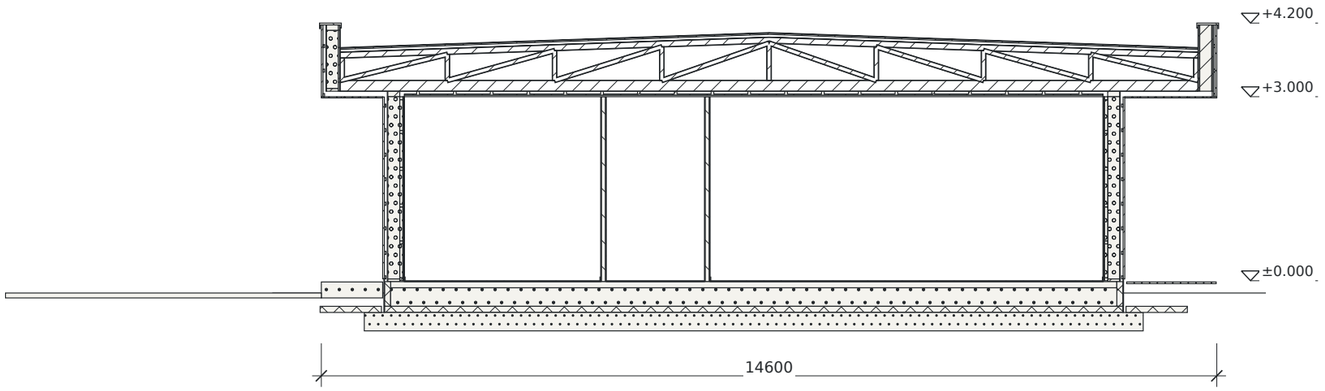

0 1 2 5 m

1:100

KONSTRUKTSIOONID

- Puitkarkass / fermid
- Mineraalvill
- Puistevill
- EPS-soojustus
- Raudbetoon
- Tihendatud liiv
- Kipsplaat

KÕRGUSSÜSTEEM

±0.000 = 86.30 m EH2000
Valmis põrand: ±0.000
Maapind: -0.200

LÕIKETASAPINNAD

A-A: mudeli Y = 7.430 m
B-B: mudeli X = 0.376 m
Lõikesuunad: vt plaan A-01

Fermid ja kihid: IFC geomeetria.
Viirutus tähistab lõigatud materjali.
Kõik mõõtkavad 1:100.

IFC4 / ARHITEKTUUR

Mõõdud millimeetrites; kõrgused meetrites.

A3 · Prindi 100% · Ära sobita lehele

EP080926 Paarismaja Karjääri tn 21a


Karjääri tn 21a, Kose alevik, Võru vald, Võru maakond

Lõiked A-A ja B-B — Eelprojekt

PROJEKTEERIJA	KUUPÄEV	MÕÕTKAVA	LEHT
Wood NDT OÜ	2026-10-28	1:100	A-02


VAATED

VAADE / IDA

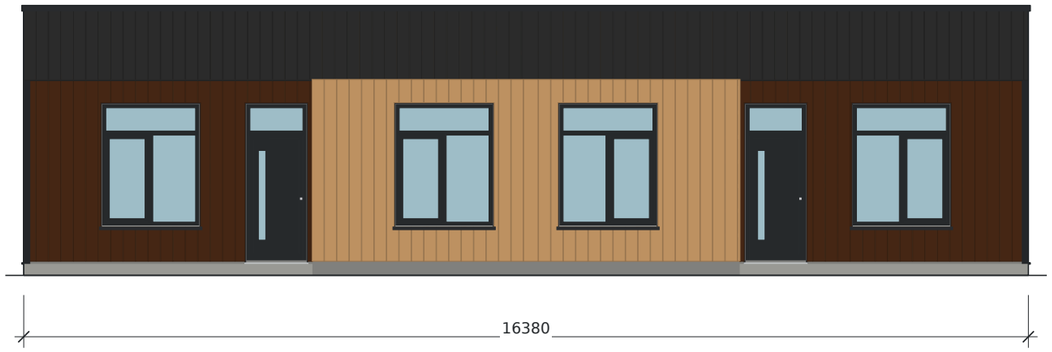


Põrand ±0.000 / Rinnatis +4.200

VAADE / LÕUNA

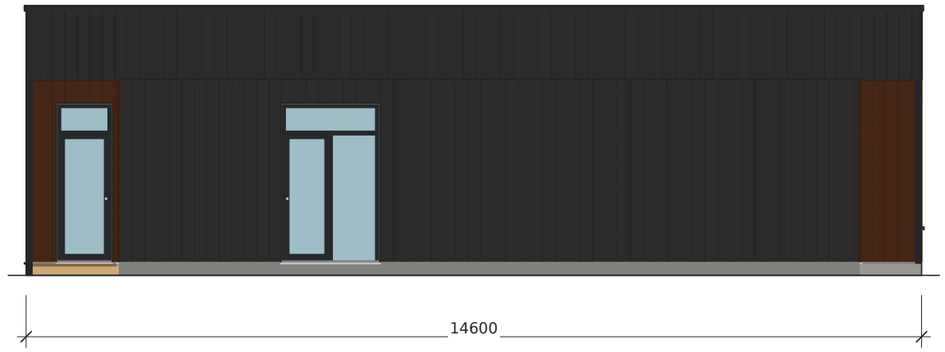


Põrand ±0.000 / Rinnatis +4.200

VAADE / LÄÄS

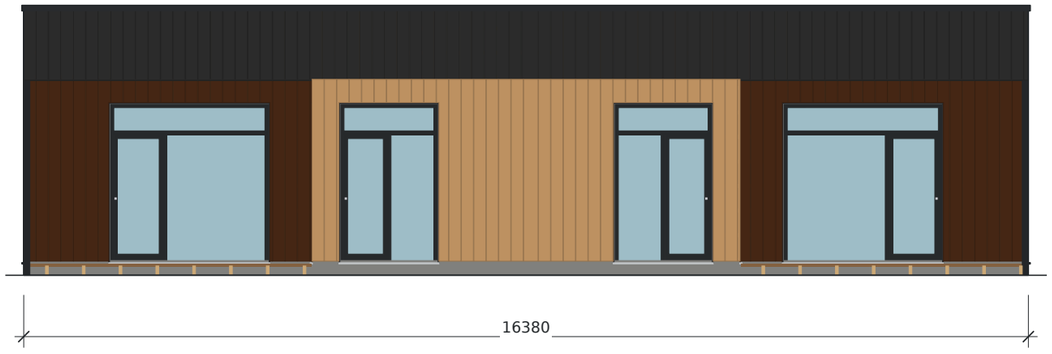

Põrand ±0.000 / Rinnatis +4.200

VAADE / PÕHI

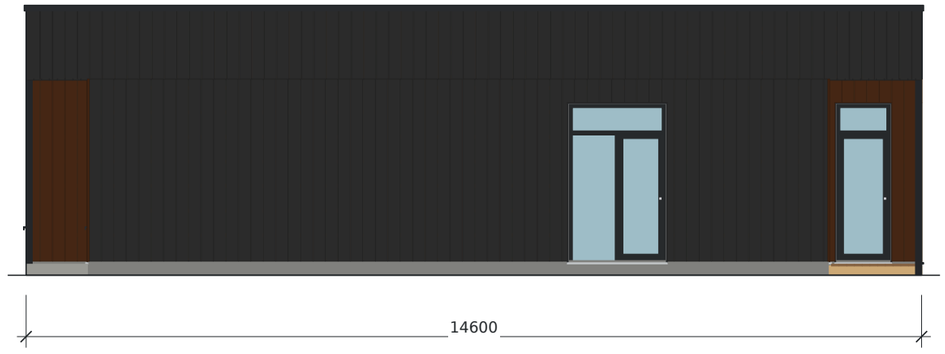

Põrand ±0.000 / Rinnatis +4.200

VÄLISVIIMISTLUS

- Naturaalne puit
- Tumepruun laudis
- Tumehall laudis
- Antratsiit raamid

IFC4 / ARHITEKTUUR

Mõõdud millimeetrites; kõrgused meetrites.

A3 · Prindi 100% · Ära sobita lehele

EP080926 Paarismaja Karjääri tn 21a

Karjääri tn 21a, Kose alevik, Võru vald, Võru maakond

Vaated — Eelprojekt

PROJEKTEERIJA	KUUPÄEV	MÕÕTKAVA	LEHT
Wood NDT OÜ	2026-10-28	1:100	A-03